


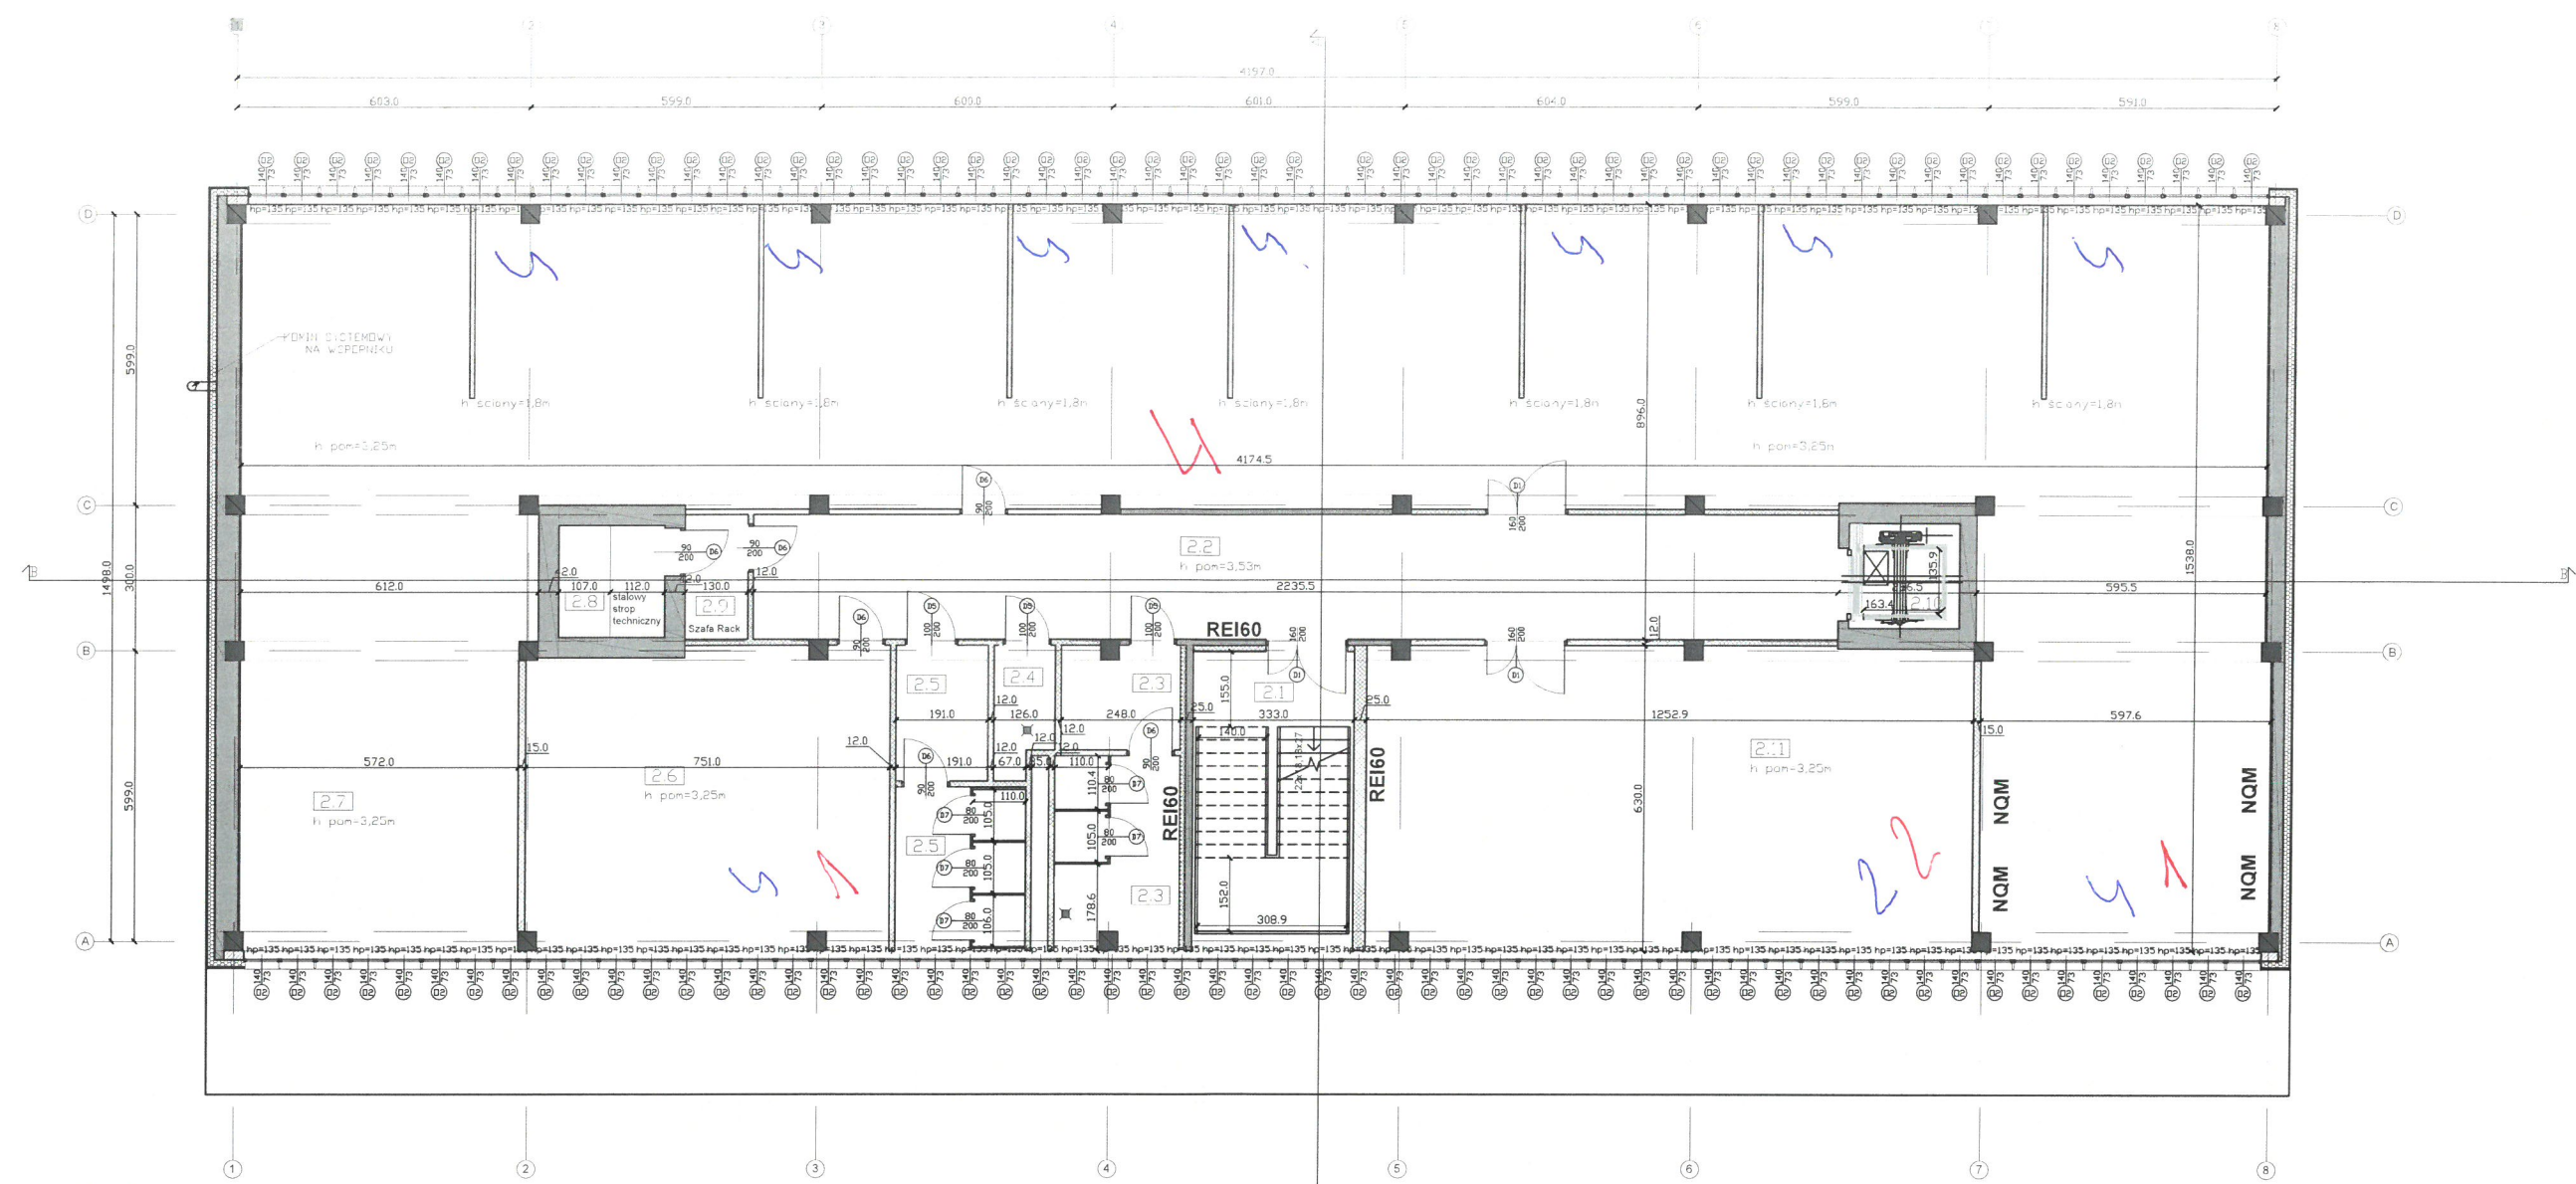

Niebieskie - IT
Czerwone - OTI

ZESTAWIENIE POWIERZCHNI - PIĘTRO 2			
Nr pom.	Nazwa pomieszczenia	Pow. [m ²]	Rodzaj posadzki
2.1	Klatka schodowa	20,98	posadzka antylektrastyczna
2.2	Korytarz	57,45	posadzka antylektrastyczna
2.3	WC Męski	15,63	posadzka ceram. - gres
2.4	MUR 2	3,15	posadzka ceram. - gres
2.5	WC Damski	14,66	posadzka ceram. - gres
2.6	Pomieszczenie konst. technol.	46,08	posadzka ceram. - gres
2.7	Warsztat montażu produkcji	366,41	posadzka antylektrastyczna
2.8	Szacht techniczny	4,93	słalowy podest
2.9	Szafa Rack	3,34	posadzka antylektrastyczna
2.10	Winda	4,90	-
2.11	Rozdzielnia pracy	78,20	posadzka antylektrastyczna
SUMA:		615,63	


LEGENDA

- ŚCIANY WEWNĘTRZNE ISTNIEJĄCE
- ŚCIANY WEWNĘTRZNE PROJEKTOWANE
- ŚCIANY WEWNĘTRZNE ISTNIEJĄCE WYMAGAJĄCE DOSTOSOWANIA DO REI60
- ŚCIANY ZEWNĘTRZNE ISTNIEJĄCE + PROJEKTOWANA IZOLACJA
- ŚCIANY ZEWNĘTRZNE PROJEKTOWANE

Uwagi:

- WSZYSTKIE WYMIARY NA RZUTACH, PRZEKROJACH, PODANO W CM; WARTOŚCI RZĘDNYCH WYSOKOŚCIOWYCH PODANO W M.
- NINIEJSZY PROJEKT BUDOWLANY SŁUŻY WYŁĄCZNIE DO CELÓW ADMINISTRACYJNYCH: ZGŁOSZENIU I UZYSKANIU DECYZJI O POZWOLENIU NA BUDOWĘ, W CELU PROWADZENIA PRAC BUDOWLANYCH NALEŻY WYKONAĆ PROJEKT WYKONAWCZY.

Nazwa inwestycji:			
PRZEBUDOWA I ROZBUDOWA BUDYNKU HALI 110			
ul. 1-go Maja 1, 02-220 Zielonka działka Nr 131 obręb 5-60-02 nr. ewid. 143402_1.0052.131			
Inwestor:			
WZE SA 1-go Maja 1, 02-220 Zielonka			
Generalny Projektant:			
ZBM S.A. ul. Cybernetyki 19B, lok. 401, 02-677 Warszawa			
Faza:	PROJEKT BUDOWLANY		
Branża:	ARCHITEKTURA		
Nazwa obiektu budowlanego:	HALA MAGAZYNOWO-PRZEMYSŁOWA		
Projektował:	mgr inż. arch Krzysztof Tomczyński MA/031/14	25.11.2024	Skala 1:100
Opracował:	mgr inż. arch. Małgorzata Szpaczyńska		
Sprawdził:	mgr inż. arch Marta Banasiak MA/100/08	25.11.2024	
Tytuł rysunku:	RZUT PIĘTRA 2		Nr.rysunku A04

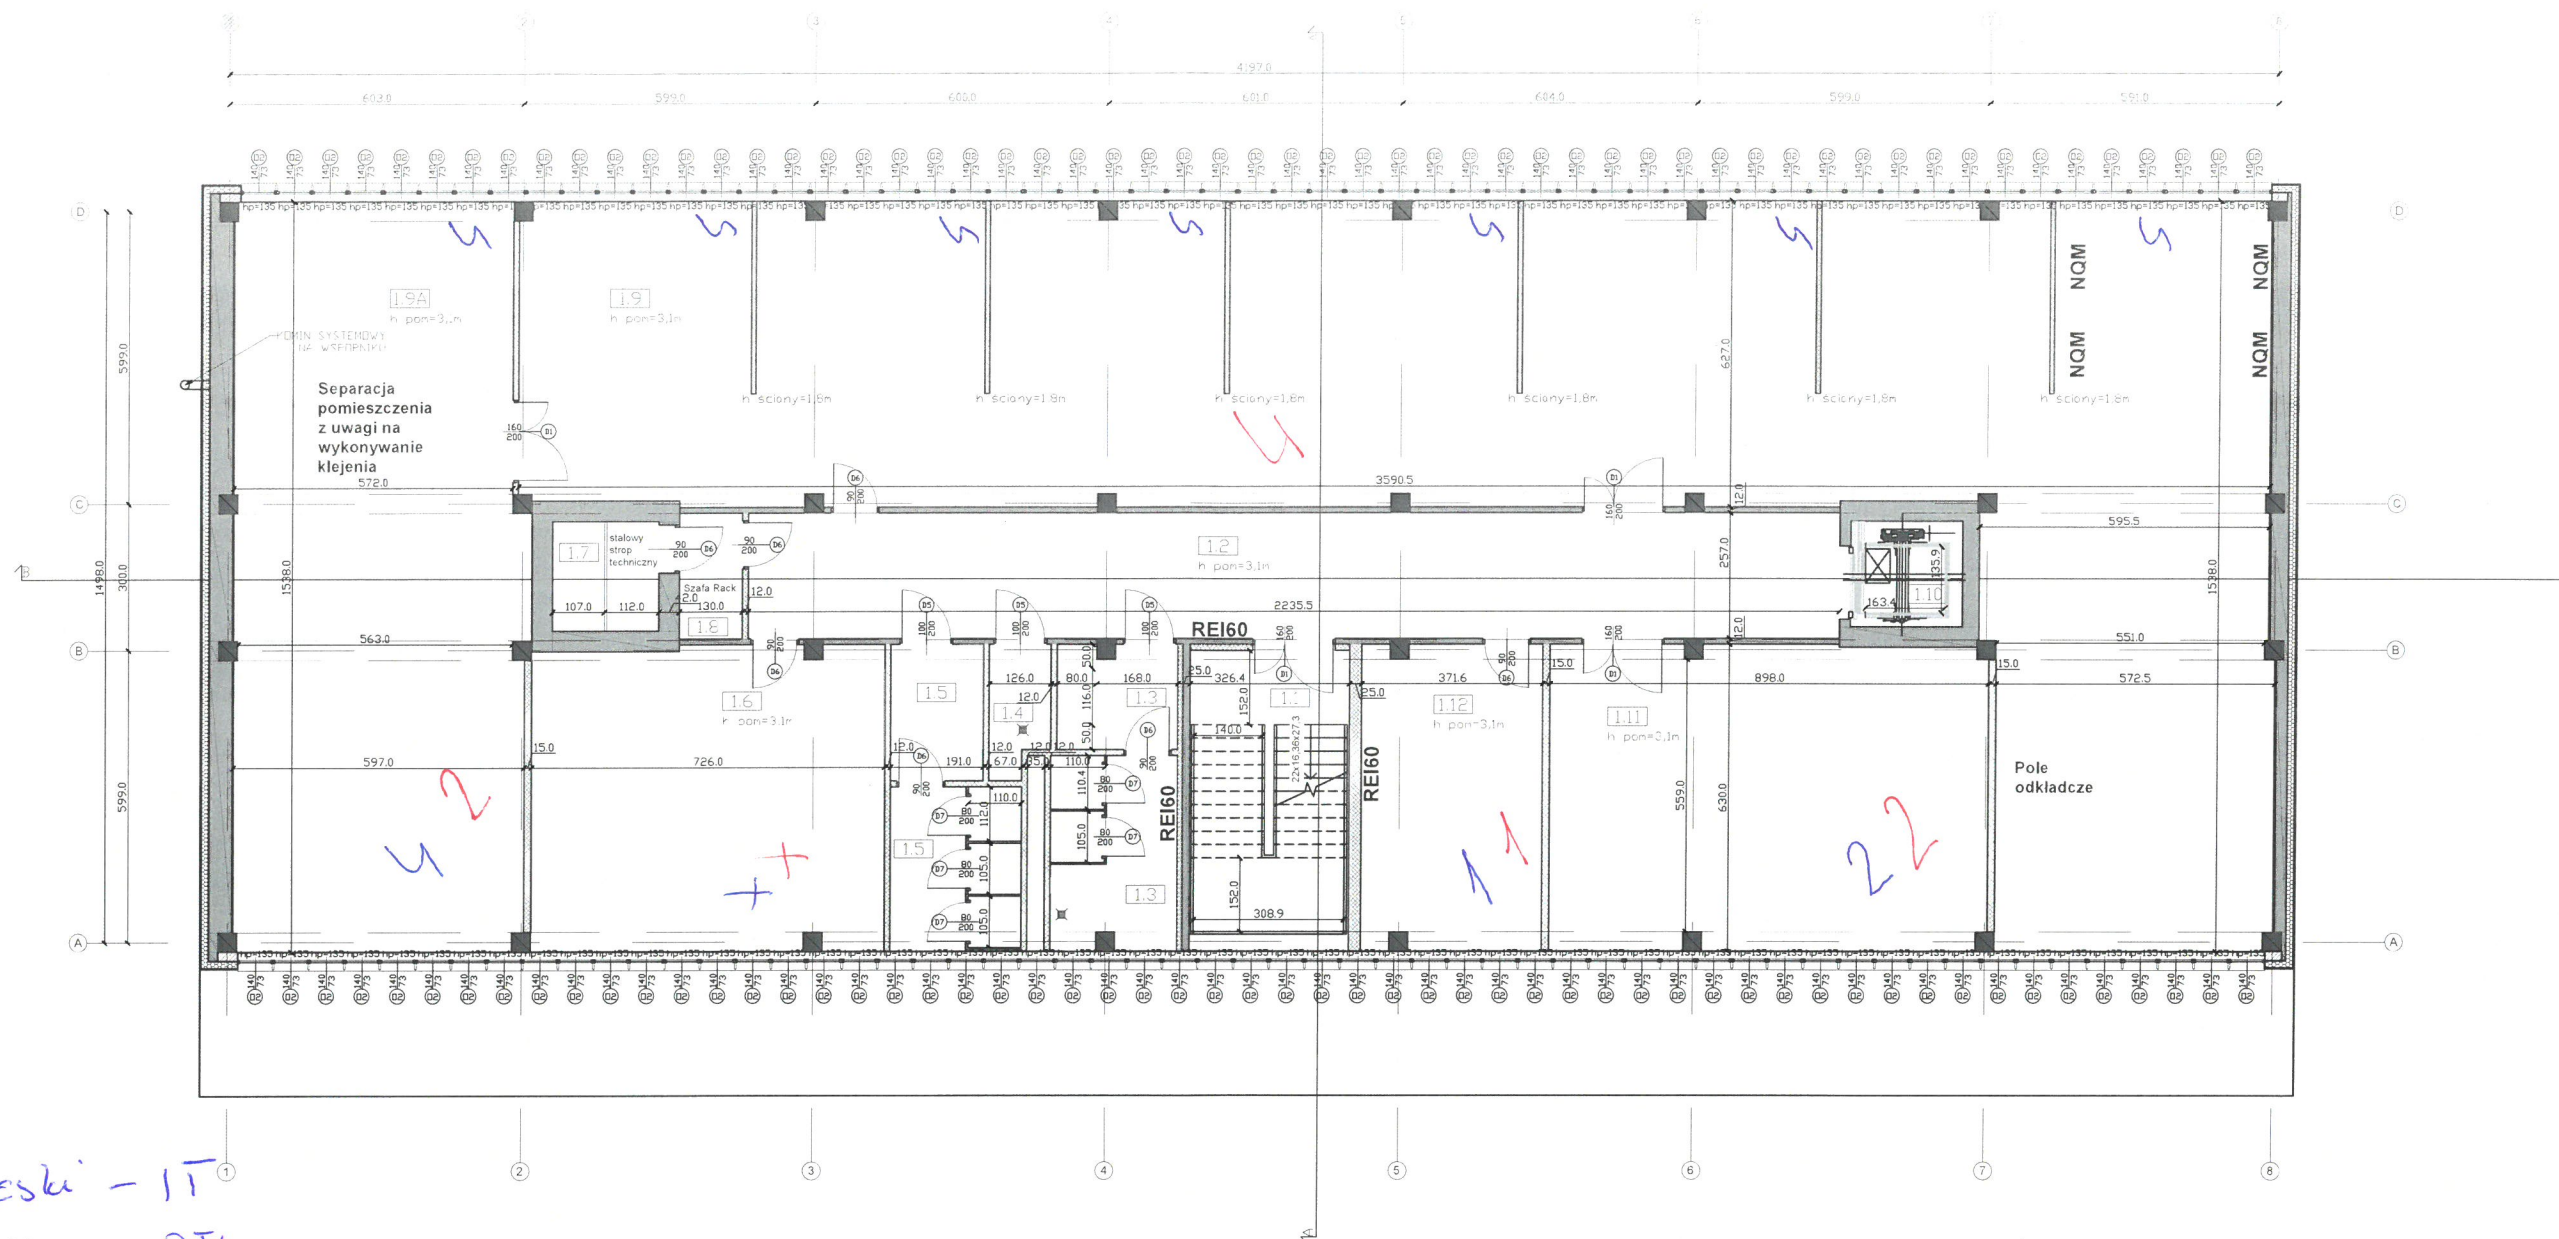

Niebieski - IT
Czerwony - OTI

ZESTAWIENIE POWIERZCHNI - PIĘTRO 1			
Nr pom.	Nazwa pomieszczenia	Pow. (m ²)	Rodzaj posadzki
1.1	Klatka schodowa	20,56	posadzka antyelektrostatyczna
1.2	Korytarz	57,45	posadzka antyelektrostatyczna
1.3	WC Męski	10,63	posadzka ceramiczna - gr. 8
1.4	WDP 1	3,15	posadzka ceramiczna - gr. 8
1.5	WC Damski	14,64	posadzka ceramiczna - gr. 8
1.6	Pomieszczenie socjalne	44,73	posadzka ceramiczna - gr. 8
1.7	Szacht techniczny	4,93	stalowy pokost
1.8	Szafa Rack	3,34	posadzka antyelektrostatyczna
1.9	Obszar montażu produkcji rodzinnej	275,30	posadzka antyelektrostatyczna
1.9A	Wydzielony obszar montażu prod. rodzinnej	98,27	posadzka antyelektrostatyczna
1.10	Winda	4,80	-
1.11	Rozdzielnia prądu	55,19	posadzka antyelektrostatyczna
1.12	Pomieszczenie dla wiewornic	23,13	posadzka antyelektrostatyczna
SUMA		613,12	


LEGENDA

- ŚCIANY WEWNĘTRZNE ISTNIEJĄCE
- ŚCIANY WEWNĘTRZNE PROJEKTOWANE
- ŚCIANY WEWNĘTRZNE ISTNIEJĄCE
- ŚCIANY WEWNĘTRZNE PROJEKTOWANE
- ŚCIANY ZEWNĘTRZNE ISTNIEJĄCE + PRZEKŁADANIE IZOLACJA
- ŚCIANY ZEWNĘTRZNE PROJEKTOWANE

Uwagi:

- WSZYSTKIE WYMIARY NA RZUTACH, PRZEKROJACH, PODANO W CM; WARTOŚCI RZĘDNYCH WYSOKOŚCIOWYCH PODANO W M.
- NINIEJSZY PROJEKT BUDOWLANY SŁUŻY WYŁĄCZNIE DO CELÓW ADMINISTRACYJNYCH: ZGŁOSZENIU I UZYSKANIU DECYZJI O POZWOLENIU NA BUDOWĘ, W CELU PROWADZENIA PRAC BUDOWLANYCH NALEŻY WYKONAĆ PROJEKT WYKONAWCZY.

Nazwa inwestycji:			
PRZEBUDOWA I ROZBUDOWA BUDYNKU HALI 110			
ul. 1-go Maja 1, 02-220 Zielonka działka Nr 131 obręb 5-60-02 nr. ewid. 143402_1.0052.131			
Inwestor:			
WZE SA 1-go Maja 1, 02-220 Zielonka			
Generalny Projektant:			
ZBM S.A. ul. Cybernetyki 19B, lok. 401, 02-677 Warszawa			
Faza:			
PROJEKT BUDOWLANY			
Branża:			
ARCHITEKTURA			
Nazwa obiektu budowlanego:			
HALA MAGAZYNOWO-PRZEMYSŁOWA			
Projektował:	mgr inż. arch. Krzysztof Tomczyński MA/031/14	25.11.2024	Skala 1:100
Opracował:	mgr inż. arch. Małgorzata Szpaczynska		
Sprawdził:	mgr inż. arch. Marta Banasiak MA/100/08	25.11.2024	
Tytuł rysunku:	RZUT PIĘTRA 1		Nr.rysunku A03

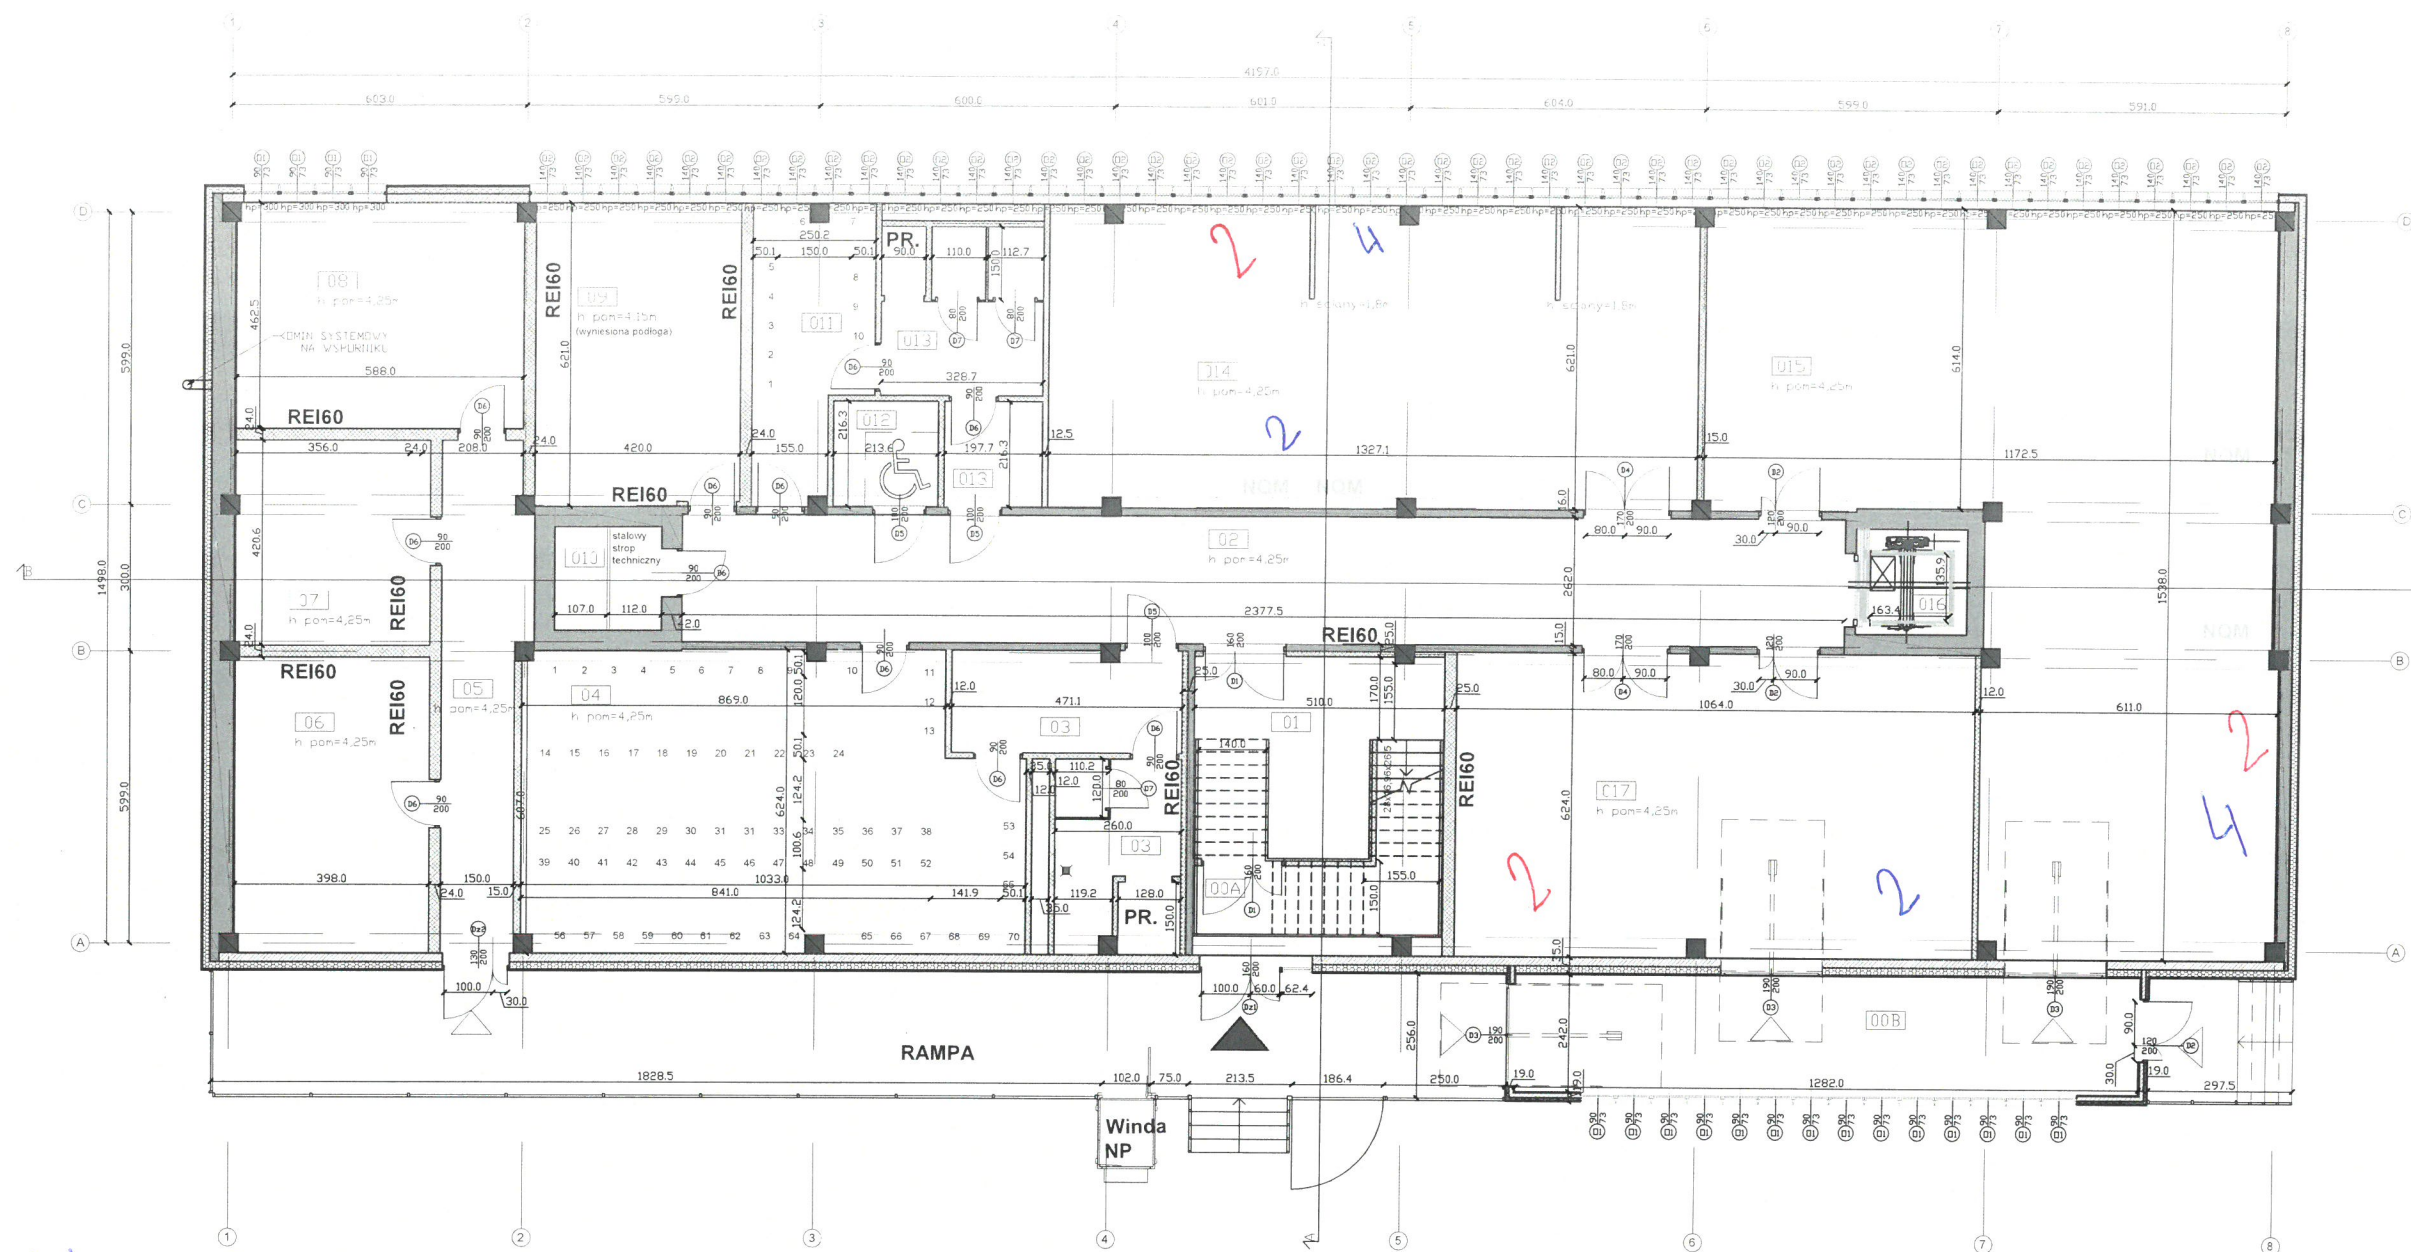

Niebieski - IT
Czerwony - OTI

ZESTAWIENIE POWIERZCHNI - PARTER			
Nr pom.	Nazwa pomieszczenia	Pow. (m ²)	Rodzaj posadzki
00A	Wiatrołap	9,00	posadzka antyelektrostatyczna
00B	Przedsiönek	33,57	posadzka antyelektrostatyczna
01	Klatka schodowa	17,86	posadzka antyelektrostatyczna
02	Korytarz	66,26	posadzka antyelektrostatyczna
03	WC męski	21,00	posadzka ceramiczna - gres
04	Szatnia męska	10,40	posadzka ceramiczna - gres
05	Korytarz	17,00	posadzka antyelektrostatyczna
06	Rozdzielnia elektryczna	24,12	posadzka antyelektrostatyczna
07	Sprezorkowania	16,70	posadzka antyelektrostatyczna
08	Kotłownia	27,09	posadzka antyelektrostatyczna
09	Serwerownia	25,95	posadzka antyelektrostatyczna
010	Szacht techniczny	4,64	posadzka antyelektrostatyczna
011	Szatnia damska	13,12	posadzka antyelektrostatyczna
012	Toileta dla osób niepełnosprawnych	4,60	posadzka antyelektrostatyczna
013	Toileta damska	15,65	posadzka antyelektrostatyczna
014	Doszar nantozu wielkogabarytowego	81,50	staowy podest
015	Doszar nantozu wielkogabarytowego	127,24	posadzka antyelektrostatyczna
016	Winda	4,80	-
017	Rozdzielnia pracy	66,13	posadzka antyelektrostatyczna
SUMA:		632,63	

LEGENDA

- SCIANY WEWNĘTRZNE ISTNIEJĄCE
- SCIANY WEWNĘTRZNE PROJEKTOWANE
- SCIANY WEWNĘTRZNE ISTNIEJĄCE WYMAGAJĄCE DOSTĄPOWANIA DO REI60
- SCIANY ZEWNĘTRZNE ISTNIEJĄCE WYMAGAJĄCE DOSTĄPOWANIA DO REI60
- SCIANY ZEWNĘTRZNE PROJEKTOWANE

Uwagi:

- WSZYSTKIE WYMIARY NA RZUTACH, PRZEKROJACH, PODANO W CM; WARTOŚCI RZĘDNYCH WYSOKOŚCIOWYCH PODANO W M.
- NINIEJSZY PROJEKT BUDOWLANY SŁUŻY WYŁĄCZNIE DO CELÓW ADMINISTRACYJNYCH: ZGŁOSZENIU I UZYSKANIU DECYZJI O POZWOLENIU NA BUDOWĘ, W CELU PROWADZENIA PRAC BUDOWLANYCH NALEŻY WYKONAĆ PROJEKT WYKONAWCZY.

Nazwa inwestycji:			
PRZEBUDOWA I ROZBUDOWA BUDYNKU HALI 110			
ul. 1-go Maja 1, 02-220 Zielonka działka Nr 131 obręb 5-60-02 nr. ewid. 143402_1.0052.131			
Inwestor:			
WZE SA 1-go Maja 1, 02-220 Zielonka			
Generalny Projektant:			
ZBM S.A. ul. Cybernetyki 19B, lok. 401, 02-677 Warszawa			
Faza:	PROJEKT BUDOWLANY		
Branża:	ARCHITEKTURA		
Nazwa obiektu budowlanego:	HALA MAGAZYNOWO-PRZEMYSŁOWA		
Projektował:	mgr inż. arch. Krzysztof Tomczyński MA/031/14	25.11.2024	Skala 1:100
Opracował:	mgr inż. arch. Małgorzata Szpoczyńska		
Sprawdził:	mgr inż. arch. Marta Banasiak MA/100/08	25.11.2024	
Tytuł rysunku:	RZUT PARTERU - WERSJA A		Nr.rysunku A02A